THE COURTS

Who's Getting Sued? No Other Newspaper Reports Every Civil Case Filing

JOHNSON COUNTY PUBLIC NOTICES

First published in The Legal Record, Tuesday, February 17, 2026.

UNCLAIMED VEHICLE AUCTION

OPEN TO THE PUBLIC

Pursuant to K.S.A. 8-1102 and K.S.A. 58-211 the following vehicles have been impounded by Lucas and Knights Towing II LLC and will be sold at public auction to the highest bidder for cash on FEBRUARY 25TH, 2026 @ 8:00 AM unless claimed by the owner and all tow, storage, and other incurred charges are paid in full.

VEHICLES CAN BE INSPECTED AT: LUCAS TOWING
1303 OTT STREET, OLATHE, KS

ALL SALES ARE FINAL WITH NO REFUNDS

TERMS OF AUCTION: All sales are final. No refunds. All sales are “as is” “where is” and there are no guarantees or warranties expressed or implied. The paperwork to obtain a new title will cost $125.00 per vehicle. There is no guarantee paperwork will obtain a new title for you in your state. Please check with the Department of Motor Vehicles in your state for details. You must agree to all sale disclosures.

Nationwide Transportation of vehicles can be arranged

2014 MAZDA MAZDA5 JM1CW2BL3E0172402
Jessica Rae Deserano

2017 HYUNDAI SONATA 5NPE24AF1HH571568
Logan B Parson
Navy Federal Credit Union

2005 CHEVROLET AVALANCHE 3GNEK12Z45G268318
Ryland Vann Ratty

2019 CHEVROLET EQUINOX 3GNAXNEV7KL148001
ANGELL CARMEN & DEAN TOD DECLUE BRAND*
BMO HARRIS BANK
NEWELL MARJORIE

2002 BUICK CENTURY 2G4WS52JX21209420
GREGG DANA
CASH COUNTRY
2/17

First published in The Legal Record, Tuesday, February 17, 2026.

Unclaimed Vehicle Auction

OPEN TO THE PUBLIC * INTERNET BIDS ONLY

Pursuant to K.S.A. 8-1102 and K.S.A. 58-211 the following vehicles will be sold at public auction on, February 25, 2026 at 07:30 pm unless claimed by the owner and all tow and storage charges are paid in full. This auction is open to the public at www.TowLot.com.

Pre-bidding begins at noon February 19, 2026 and continues until the live internet sale begins at 07:30 pm February 25, 2026.

Vehicles can be inspected at **Pro-Tow L.L.C. / Overland Tow Service Inc. 3505 Merriam Drive, Overland Park, KS** starting February 19, 2026, thru February 25, 2026 from 9 am to 5 pm weekdays.

Terms of Auction: **ALL SALES ARE FINAL NO REFUNDS! ONLY REGISTERED USERS OF www.TowLot.com MAY BID ON VEHICLES. This sale is by internet bid only!**

All sales are “**AS IS**” AND “**WHERE IS**” there are **NO GUARANTEES OR WARRANTIES.** Paperwork to obtain title is $150.00 per vehicle. There is **NO GUARANTEE** the paperwork we provide will obtain a title for you in your state. Please check with your state for title requirements. You must agree to all sale disclosures and be registered user of **www.TowLot.com** to qualify as a bidder for this sale.

Pro-Tow L.L.C. at 913-262-3300

2	2010 Hyundai ELANTRA	KMHDU4AD2AU907594
3	2009 Chevrolet Cobalt	1G1AT58H497285902
4	2012 Chevrolet Impala	2G1WF5E37C1336139
5	1999 Ford Taurus	1FAFP53U1XA161694
6	2018 Jeep Compass	3C4NJCCB8JT358761
7	1998 Ford F-150	1FTZX1769WNA34694
8	2019 Lincoln MKZ	3LN6L5C93KR607758
9	2015 Toyota RAV4	2T3YFREV9FW134231
10	2005 Ford Taurus	1FAFP53275A157791
11	2007 Saturn Aura	1G8ZS57N37F226213

2/17

First published in The Legal Record, Tuesday, February 17, 2026.

The City of Merriam is seeking bids for the Carter Ave. (67th to Carter) Street Improvements Project. The project includes a mill and overlay with full depth pavement replacement, stormwater improvements, and sidewalk installation. Plans can be downloaded from Drexel at www.drexeltech.com.

2/17

JOHNSON COUNTY PUBLIC NOTICES

First published in The Legal Record, Tuesday, February 17, 2026.
USD 232 Department of Student Nutrition Notice of 2026-2027 Request for Proposals
The USD 232 Student Nutrition Department is soliciting proposals for goods needed for the 2026-2027 school year. The following request for proposals are now being accepted.

Pizza – Department of Student Nutrition
USD 232 proposes to contract with a vendor to furnish and deliver ready-to-eat pizza to individual school food service operating sites of Mill Valley High School and De Soto High School to meet the National School Lunch Program regulations for the daily menu and ala carte sales.
All responses due March 9 by 2:30 pm

Ala Carte Beverage Products – Department of Student Nutrition
USD 232 proposes to contract with a vendor to furnish and deliver ala carte beverages that meet the USDA Smart Snacks in Schools Guidelines to individual school food service operating sites.
All responses due March 9 by 2:45 pm

Smoothies – Department of Student Nutrition
USD 232 proposes to contract with a vendor to furnish and deliver ala carte smoothies to individual school food service operating sites of Mill Valley High School and De Soto High School that meet the USDA Smart Snacks in Schools guidelines.
All responses due March 9 by 3:00 pm

Chicken Sandwiches – Department of Student Nutrition
USD 232 proposes to contract with a vendor to furnish and deliver ready-to-eat breaded chicken sandwiches to individual school food service operating sites of Mill Valley High School and De Soto High School one time per month through the school year to meet the National School Lunch Program regulations for the daily menu and ala carte sales.
All responses due March 9 by 3:15 pm

To obtain a copies of the detailed request for proposals please visit the USD 232 Student Nutrition webpage at the following link: https://www.usd232.org/departments/student-nutrition/departments/student-nutrition/food-service-rfps Additionally, you may contact the Director of Student Nutrition, Jolyn Baldner at jbaldner@usd232.org or 913-667-6200 for copies and questions.
2/17

First published in The Legal Record, Tuesday, February 17, 2026.

NOTICE TO BIDDERS
CITY OF PRAIRIE VILLAGE, KANSAS
2026 UBAS PROGRAM | SOMERSET, STATE LINE TO MISSION

Sealed bids will be received by the City Governing Body of Prairie Village, Kansas at the office of City Clerk at the City Hall, 7700 Mission Road, Prairie Village, Kansas, until

3:00 p.m. (CST) on MARCH 4, 2026.

All bids shall be submitted in an envelope stamped "Bid", sealed and addressed to the City Clerk, and marked and online in VPM via www.virtual-bid.com/bids-search/01j7ycp3bc1a0h49r0nag4r10k.

2026 UBAS PROGRAM | SOMERSET, STATE LINE TO MISSION

At the above stated time and place, all bids shall be publicly opened and read aloud. Bids received after the designated closing time will be returned unopened.
The project includes, but not limited to,

UBAS WITH MINOR REPAIRS TO PAVEMENT, CURB AND SIDEWALK.

All equipment, material and workmanship must be in accordance with the Bid Documents, Plans, Project Manual and Contract Documents on file with the City Clerk, Prairie Village, Kansas. Copies of the Bid Documents, Plans, Project Manual, and Contract Documents may be obtained at no cost from the City of Prairie Village Public Works Department at www.pvkansas.com.

Non-resident corporations that are not already registered with the Kansas Secretary of State and all non-resident individuals and partnerships are required by law to register with the Director of Revenue, State Office Building, Topeka, Kansas, and to pay a fee of Ten Dollars ($10.00) for each and every contract as a precedent to commencing work on the contract. For contracts in excess of Ten Thousand Dollars ($10,000), the foreign contractor shall file with the Director of Revenue an acceptable bond for ten percent (10%) of the contract.

CITY OF PRAIRIE VILLAGE
ADAM GEFFERT, CITY CLERK

2/17

First published in The Legal Record, Tuesday, February 17, 2026.

REQUEST FOR PROPOSALS
CITY OF GARDNER

The City of Gardner is requesting proposals from vendors with expertise in pavement assessment and pavement management to perform a Pavement Condition Index (PCI) survey to analyze and inventory the existing conditions of all City maintained roadways. In addition to the PCI, the selected firm will develop and furnish a Pavement Management Program to provide recommendations to optimize short-term and multi-year street maintenance and reconstruction projects based on available budget scenarios. Proposals will be accepted by the City of Gardner, Kansas, Attn: City Clerk, 120 E. Main Street, Gardner, Kansas, 66030, until **10:00 A.M.** (local time) on **March 10, 2026**.
Additional information may be obtained via the city's website, www.gardnerkansas.gov
2/17

JOHNSON COUNTY PUBLIC NOTICES

First published in The Legal Record, Tuesday, February 10, 2026.

RESOLUTION NO. 2026-005

A RESOLUTION PROVIDING NOTICE AND CALLING FOR A PUBLIC HEARING TO APPEAR AND SHOW CAUSE WHY THE STRUCTURE AT 7730 NOLAND ROAD SHOULD NOT BE CONDEMNED AND ORDERED REPAIRED OR DEMOLISHED AS AN UNSAFE OR DANGEROUS STRUCTURE IN ACCORDANCE WITH K.S.A. 12-1750 ET. SEQ.

WHEREAS, on August 10, 2025, a fire damaged the structure located at 7730 Noland Road; and

WHEREAS, pursuant to K.S.A. 12-1750 et seq., the Governing Body has the power to cause the repair or removal of, or to remove any structure located within the City which is determined to be unsafe or dangerous; and

WHEREAS, if necessary, the City may recover costs for the repair and removal of an unsafe or dangerous structure in accordance with the Lenexa City Code Article 1-9-H and K.S.A. 12-1755; and

WHEREAS, pursuant to K.S.A. 12-1752, the City of Lenexa Building Codes Administrator has determined the structure located at 7730 Noland Road to be unsafe and dangerous and filed a written statement, of such determination with the Governing Body on February 3, 2026; and

WHEREAS, Pursuant to K.S.A. 12-1752, the Governing Body shall provide notice and call for a public hearing for the owner, owner's agent and any lienholders of record to appear and show cause why the structure should not be condemned and ordered repaired or demolished as an unsafe or dangerous structure; and

WHEREAS, pursuant to this notice and in accordance with K.S.A. 12-1752 et seq., the City may ultimately repair or demolish such structure and the owner may lose any interest in the salvage proceeds of such structure and that any costs borne by the City in excess of the salvage value may be assessed against the real property.

NOW, THEREFORE, BE IT RESOLVED BY THE GOVERNING BODY OF THE CITY OF LENEXA, KANSAS:

SECTION ONE: This resolution shall become effective upon adoption by the Governing Body.

SECTION TWO: This Resolution shall be published once each week for two consecutive weeks on the same day of each week in the official City newspaper.

SECTION THREE: The public hearing shall be held by the Lenexa Governing Body on April 7, 2026, at 7:00 p.m. or as soon thereafter as it can be heard, at Lenexa City Hall, 17101 West 87th Street Parkway, Lenexa, Kansas, 66219.

SECTION FOUR: The Building Codes Administrator is hereby directed to mail a copy of this resolution by mail to the owner, owner's agent, any lienholders and occupants of record within three days following the first publication hereof, all in accordance with K.S.A. 12-1752.

ADOPTED by the Lenexa City Council this 3rd day of February, 2026.

SIGNED by the Mayor this 3rd day of February, 2026.

CITY OF LENEXA, KANSAS

/s/ Julie Sayers
Julie Sayers, Mayor

[SEAL]

Attest:

/s/ Jennifer Martin
Jennifer Martin, City Clerk

Approved As To Form:

/s/ Steven D. Shrout
Steven D. Shrout, Assistant City Attorney
2/10 2/17

First published in The Legal Record, Tuesday, February 10, 2026.

Marvin's Tow Service
20160 W 191st St
Spring Hill, KS 66083
Auction will be held on 03/01/2026 at 11:00am

2021	Freightliner	Cascadia	Red	3AKJHHDRXMSMG7928
1997	Ford	Ranger	Red	1FTCR14X2VPB19330
2001	Honda	Civic	Silver	2HGES16561H515608
2005	Toyota	Sienna	Red	5TDZA22C85S381334
2007	Hyundai	Tiburon	White	KMHHN66F27U234982
2006	Volkswagen	New Beetle	White	3VWRW31C66M407825
2013	Toyota	Sienna	Gray	5TDKK3DC2DS293847
2017	GMC	Sierra 2500 HD	Silver	1GT12TEY1HF144986
2008	Dodge	Grand Caravan	White	2D8HN54PX8R737444
2012	Ford	F-150	White	1FTEX1EM9CFB42707
2008	Ford	Fusion	Silver	3FAHP07Z38R149023
2020	YongFu	YN50QT-5	Black	LL0TDNPE8LY920549
1998	Toyota	Camry	Gray	4T1BG22K5WU259174
1996	Oldsmobile	Eighty-Eight	Gray	1G3HY52K1T4802853
2014	Kia	Optima	Black	5XXGM4A70EG281826
2008	Ford	F-350 Super Duty	Black	1FTSX31R38EA35374
2011	Chevy	Impala	White	2G1WF5EKXB1164808
2014	Ford	Edge	Blue	2FMDK3GCXEBA82981
2007	Chrysler	PT Cruiser	Black	3A4FY48B97T534315
2000	Toyota	Camry	Maroon	4T1BG22K1YU692803
2010	Peterbilt	386-Series	Blue	1XPHD49X8AD793748
2011	Chevy	Impala	Red	2G1WA5EK2B1194318
1999	Toyota	Camry	Tan	4T1BF28K0XU074817
2007	Toyota	4 Runner	Black	JTEBU14R978094754
2010	Volkswagen	Jetta	White	3VWRZ7AJ1AM071684
2004	Buick	LeSabre	White	1G4HP54K144154587
2002	Lexus	LS 430	Gold	JTHBN30F920090332
2013	BMW	3 Series	White	WBA3B5G51DNS02129
2008	Chevrolet	Tahoe	Gold	1GNFK13098J160137
2012	Cadillac	CTS	Silver	1G6DP8E34C0150859
2003	Toyota	4Runner	Blue	JTEZU14R630003320
2002	Toyota	Tacoma	White	5TENL42N22Z888332
2020	Dodge	Journey	Silver	3C4PDCGB5LT268772
2013	Chevrolet	Impala	Black	2G1WC5E36D1254073
2015	Dodge	Dart	Silver	1C3CDFAA7FD213206
2006	Audi	A4	Black	WAUDT48H56K006333
1995	Great Dane	Trailer	White	1GRAA0626SB138004
2005	Ford	F-150	White	1FTRF02W05KC49014
2012	Ford	Fusion	Blue	3FAHP0HA8CR334573
2011	Toyota	Camry	Black	4T4BF3EK5BR210383
2003	Ford	Focus	White	1FAFP363X3W227552
1995	Great Dane	Trailer	White	1GRAA0626SB138164
2005	Hino	268	White	5PVNB8JK51S11147
2007	International	Durastar 4300	White	1HTMMAAL07H470693
2015	International	Durastar 4300	White	1HTMMAAL2FH509086
2013	Chrysler	200	Gray	1C3CCBBG6DN558149
2014	Chevrolet	Cruze	Black	1G1PC5SB1E7427017
2003	Kia	Sorento	White	KNDJC733335066186
1999	Honda	Civic	Black	1HGEJ8149XL032779
2002	Acura	RSX	Black/White	JH4DC53832C025305

2/10 2/17

First published in The Legal Record, Tuesday, February 3, 2026.

JOHNSON COUNTY, KANSAS
GENERAL NOTICE TO BIDDERS

Notice is hereby given that Johnson County, KS provides notifications for its formal Invitation to Bids, Request for Proposals, and other solicitations at https://jocogov.ionwave.net. Copies of these documents and the required submittal forms are available either through this website or at the location noted online. Please call 913-715-0525 should you have any questions.

The County is an Equal Opportunity Employer and will not do business with any firm or individual that any way, directly or indirectly, discriminates against any person of a Protected Status or other circumstance prohibited by federal, state or local law, rule or regulation.
2/3 2/10 2/17 2/24

First published in The Legal Record, Tuesday, February 17, 2026.
Johnson County Community College (JCCC)
Procurement Services
12345 College Blvd, CSB 170
Overland Park, KS 66210
JCCC is accepting proposals for: **RFP# 26-211 Comprehensive Employee Compensation & Classification Study: Faculty**. Solicitation documents may be obtained via the College's eProcurement site and public bulletin board, ProcureWare https://jccc.procureware.com/home. Call 913-469-3812 or email procurement@jccc.edu if you have questions or need assistance. Bids must be received through ProcureWare no later than March 11, 2026, 2:00pm CST. Upon completion of evaluation ProcureWare will be updated with contract award information.
2/17

First published in The Legal Record, Tuesday, February 17, 2026.
Johnson County Community College (JCCC)
Procurement Services
12345 College Blvd, CSB 170
Overland Park, KS 66210
JCCC is accepting proposals for: **RFP# 26-212 Comprehensive Employee Compensation & Classification Study: Staff**. Solicitation documents may be obtained via the College's eProcurement site and public bulletin board, ProcureWare https://jccc.procureware.com/home. Call 913-469-3812 or email procurement@jccc.edu if you have questions or need assistance. Bids must be received through ProcureWare no later than March 11, 2026, 2:00pm CST. Upon completion of evaluation ProcureWare will be updated with contract award information.
2/17

JOHNSON COUNTY PUBLIC NOTICES

First published in The Legal Record, Tuesday, February 17, 2026.

ORDINANCE NO. Z-4386

REZONING NO. REZ2025-00012

AN ORDINANCE RELATING TO ZONING: AMENDING CERTAIN ZONING REGULATIONS SHOWN ON SHEET NO. 09 OF THE ZONING DISTRICT MAP INCORPORATED BY REFERENCE BY OVERLAND PARK MUNICIPAL CODE SECTION 18.150.020; AMENDING OVERLAND PARK MUNICIPAL CODE SECTION 18.150.020, AND REPEALING THE SAME.

BE IT ORDAINED BY THE GOVERNING BODY OF THE CITY OF OVERLAND PARK, KANSAS:

Section 1. Amendment of Zoning District Map. The zoning district boundaries set forth on the Zoning District Map, Sheet No. 09, of the City of Overland Park, Kansas, incorporated by reference in the Overland Park Municipal Code, Section 18.150.020, are hereby amended with respect to the following described real property, to-wit:

Legal Description:

All of Lots 19 through 30, Block 10, Elmhurst, a subdivision of land in the City of Overland Park, Johnson County Kansas. Except that part therefore dedicated for street purposes.

The real property hereinabove described shall hereafter be deemed zoned and classified as MXD, Planned Mixed-Use District.

The Zoning District Map, Sheet No. 09 is hereby ordered to be changed to reflect such amendment.

Section 2. Stipulations and Conditions. The rezoning granted in Section 1 of this ordinance is hereby made contingent upon the performance and observance of the following regulations, stipulations, conditions, and restrictions, to-wit:

a. The development shall be in accordance with Exhibit "A" (Site Plan), and Exhibit "B" (Building Elevations), which are filed in the office of the Planning Commission Secretary at City Hall and which are incorporated by reference as if set out in full herein. Provided, subsequent revisions may be made thereto in accordance with the application, notice, and other requirements of O.P.M.C. Title 18. In addition, the development shall follow and comply with all regulations and standards of the City of Overland Park unless specifically exempted by the Governing Body.

b. Development of the site shall be limited to the following:

- 6,440 square feet of retail
- 29 multi-family units

Modifications to the plan and proposed square-footage/units may be allowed per Section 18.140.200 of the Unified Development Ordinance.

c. Prior to the issuance of a building permit, the property shall be preliminary and final platted.

d. Prior to the submittal of a building permit, the Planning Commission shall approve final development plans. The Project Design Manual as required in MUDS 4.7 shall also be submitted and approved as part of the final development plan review.

e. Prior to the issuance of a certificate of occupancy, all rooftop and ground-mounted mechanical equipment shall be screened from view with an architectural treatment that is compatible with the building architecture.

f. Prior to the issuance of the first final development plan, the applicant shall meet with the city forester to discuss specific tree preservation measures to be undertaken prior to and during construction to preserve identified trees. The construction documents for such permits shall include the recommendations of the city forester. Existing trees along the perimeter of the plan shall be preserved/protected to the extent possible.

g. Concurrent with the submittal of construction plans, the applicant shall provide a separate copy of the landscape plan/tree preservation plan for review by the city forester.

h. The final plan shall meet the requirements of the Site Design Standards, Architectural Design Standards, and Mixed-Use Standards.

i. A deviation is approved from MUDS Section 5.3.2. to allow for a front yard setback to be located 12.3 feet from the property line.

j. At the time of building permit review, the applicant shall provide the locations of exterior fire department connections. These connections shall not be obstructed by landscaping, walls, or other barriers and shall meet Section 912.3.2 of the Overland Park Fire Code. These locations are subject to review by the Overland Park Fire Department.

k. This project is required to comply with the Overland Park Municipal Code Section 16.100.1010.4 for physical security. Please contact the Building Safety Division at (913) 895-6225 for more information.

l. The number, location, and geometrics of all driveways and parking areas are subject to review and approval by the Planning and Development Services Department.

m. Prior to the issuance of a site development or building permit, the developer's engineer shall provide a Final Stormwater Management Study that addresses any outstanding items from the Preliminary Stormwater Management Study and includes any design changes. The study shall be approved prior to the issuance of a permit.

n. Prior to the issuance of a certificate of occupancy for any phase of the project requiring stormwater detention, the detention facility serving this development shall be certified by the design engineer, a professional engineer, licensed in the State of Kansas.

o. Prior to the issuance of a certificate of occupancy, the detention facility serving the site shall be constructed and in service.

p. Prior to the approval of a public improvement permit, the owner/developer shall submit a detention maintenance agreement for review and approval by the Engineering Services Division. The document shall address future maintenance of the private detention control structure located on the public storm sewer system. The detention maintenance agreement shall be submitted to the Engineering Services Division for recording at the Johnson County Department of Records and Tax Administration with the recording fee paid by the owner/developer.

q. Prior to the issuance of a certificate of occupancy, all sidewalk ramps in the public right-of-way adjacent to the property shall be constructed or reconstructed to conform with current public sidewalk ramp requirements, including the installation of truncated domes where applicable.

r. Prior to the issuance of a certificate of occupancy, any existing public sidewalk or public trail adjacent to this property that does not substantially meet current City standards or is in poor condition shall be reconstructed to current City standards. The limits of the repair shall be approved by the Engineering Services Division prior to the issuance of a building or site development permit. An alternate route for pedestrian traffic shall be maintained in compliance with Section 13.10.070 of the Municipal Code. In no case shall public sidewalks be closed to pedestrian traffic for a period exceeding 30 days without prior approval from the City.

s. Prior to the issuance of a certificate of occupancy, all new private sidewalks shall comply with the City's standard details for private sidewalks and sidewalk ramps, unless waived by the Director of Planning and Development Services (Section 18.120.015). Noncompliant pedestrian routes shall be clearly identified on the plans and comply with the building code.

t. Prior to the issuance of a certificate of occupancy for any adjacent building, a five-foot wide public sidewalk shall be constructed along the 87th Street frontage of the parcel containing the building.

Section 3. The Zoning District Map for the City of Overland Park, Kansas, is hereby amended by this ordinance, Ordinance No. Z-4386, said amendment being incorporated by reference pursuant to Section 18.150.020 which is amended to read as follows:

18.150.020 Zoning District Map
The boundaries of the zoning districts enumerated in Section 18.150.010 and in Article 7 of the Johnson County, Kansas, Zoning & Subdivision Regulations adopted herein shall be shown on a map officially designated as the Zoning District Map, which map is hereby incorporated by reference. Such "Zoning District Map" shall be marked "official copy of zoning district map incorporated into the zoning regulations by adoption of a zoning ordinance by the Governing Body of the City on the 2nd day of February, 2026," and shall be filed in the office of the Director of Planning and Development Services of the City of Overland Park, Kansas, to be open to inspection and available to the public at all reasonable business hours. Ordinances amending the boundaries of zoning districts shall order the "Zoning District Map" to be changed to reflect such amendment, shall amend this Section 18.150.020, and shall reincorporate such "Zoning District Map" as amended.

Section 4. All zoning ordinances or provisions of the City of Overland Park, Kansas, otherwise limiting the use of the above described real property and inconsistent with this ordinance are hereby repealed. Further, Overland Park Municipal Code, Section 18.150.020, is hereby repealed to allow for amendment to the Zoning District Map as set forth hereinabove.

Section 5. Take Effect. This ordinance shall take effect and be in force as of the date of its passage, approval and publication as provided by law.

[Remainder of Page Intentionally Left Blank]

PASSED by the City Council this 2nd day of February, 2026.

APPROVED by the Mayor this 2nd day of February, 2026.

CITY OF OVERLAND PARK, KANSAS

By: (s) Curt Skoog
Curt Skoog
Mayor

CONTINUED ON NEXT PAGE

JOHNSON COUNTY PUBLIC NOTICES

CONTINUED FROM PRECEDING PAGE

(SEAL)

ATTEST:

By: (s) Elizabeth Kelley
Elizabeth Kelley
City Clerk

APPROVED AS TO FORM:

By: (s) Stephen B. Horner
Stephen B. Horner
Senior Assistant City Attorney

2/17

First published in The Legal Record, Tuesday, February 17, 2026.

RESOLUTION NO. 915

A RESOLUTION declaring the necessity and authorizing a survey and descriptions of lands necessary to be condemned for a utility easement for the location, installation, placement, operation, inspection, maintenance, repair and replacement of street lighting, electric structures and lines, water mains and lines, sanitary mains and lines, stormwater collection inlets, mains and lines, telecommunication lines and other public utilities and appurtenances at 6220 Antioch Road.

NOW, THEREFORE, BE IT RESOLVED by the City Council of the City of Merriam, Kansas:

Section 1. It is hereby found and determined necessary that certain lands and/or interests in lands be condemned for public use for the location, installation, placement, operation, inspection, maintenance, repair and replacement of street lighting, electric structures and lines, water mains and lines, sanitary mains and lines, stormwater collection inlets, mains and lines, telecommunication lines and other public utilities and appurtenances at 6220 Antioch Road.

Section 2. The City Council hereby directs and authorizes the City Attorney and the City Public Works Director to cause a survey and description of such parcels to be undertaken and filed with the City Clerk; to thereafter prepare and submit to the City Council an ordinance authorizing the exercise of eminent domain with respect to such parcels; and upon approval of the same by the City Council to initiate eminent domain proceedings in the District Court of Johnson County, and to undertake all other necessary actions to complete acquisition of such parcels.

Section 3. This Resolution is effective upon its adoption by the City Council and its publication in the official City newspaper.

APPROVED BY THE CITY COUNCIL OF THE CITY OF MERRIAM, KANSAS THIS 9th DAY OF FEBRUARY, 2026.

Bob Pape
Bob Pape
Mayor

ATTEST:
Julianna Pinnick
City Clerk

APPROVED AS TO FORM:
Katuyt Dumovich
~~Ryan Denk~~ Kathryn Dumovich
City Attorney

2/17

First published in The Legal Record, Tuesday, February 10, 2026.

NOTICE OF PUBLIC AUCTION

· 2017 Ford Focus - 1FADP3F21HL294211

The above vehicles will be sold at public auction on February 27, 2026 at 8:00am, unless claimed by owner and all repair and storage fees are paid in full. Auction location is 11826 West 112th Street, Overland Park, KS 66210
2/10 2/17 2/24

First published in The Legal Record, Tuesday, February 17, 2026.

CITY OF SHAWNEE

ORDINANCE NO. 3543

AN ORDINANCE ADOPTING THE SHAWNEE, KANSAS, 2026 Achieve shawnee COMPREHENSIVE PLAN amendments

WHEREAS, the Planning Commission of the City of Shawnee has previously adopted the Comprehensive Plan for the City pursuant to the authority granted by Kansas Statutes; and

WHEREAS, pursuant to K.S.A. 12-747, the Comprehensive Plan adopted by the Planning Commission through resolution, and any amendments must be adopted by the Governing Body; and

WHEREAS, a copy of the Achieve Shawnee Comprehensive Plan, including the 2026 amendments, adopted by the Planning Commission, together with a written summary of the Public Hearing thereon held by the Planning Commission, has been submitted to the Governing Body.

NOW THEREFORE, BE IT ORDAINED BY THE GOVERNING BODY OF THE CITY OF SHAWNEE, KANSAS:

PARAGRAPH 1. The Governing Body of the City of Shawnee, Kansas, hereby adopts the Achieve Shawnee Comprehensive Plan, 2026 Edition, as amended and approved by the Planning Commission pursuant to Resolution of the Planning Commission dated February 2, 2026 (to be known as the Achieve Shawnee Comprehensive Plan, 2026 Edition). The amendments adopted by this ordinance are as follows:

1. Section 3, Future Land Use Framework map amendments for:
   - 7700 Block of Renner Road as described in the Planning Commission staff report dated 2/2/2026,
   - Northeast corner of 75th Street and K-7 Highway as described in the Planning Commission staff report dated 2/2/2026,
   - West side of K-7 Highway from Clear Creek Parkway north to the Oak Valley Shopping Center as described in the Planning Commission staff report dated 2/2/2026.

PARAGRAPH 2. There is hereby incorporated by reference the City of Shawnee, Achieve Shawnee Comprehensive Plan, 2026 Edition, prepared, compiled, published and promulgated by the Community Development Department of the City of Shawnee, in form as defined in K.S.A. 12-3301(c), such incorporation by reference being authorized by K.S.A. 12-3009 to and including 12-3012. At least one copy of this Ordinance No. 3543 shall be attached to a copy of the City of Shawnee, Achieve Shawnee Comprehensive Plan, 2026 Edition, marked as or stamped "official copy as incorporated by Ordinance No. 3543" and shall be filed with the City Clerk to be open to inspection and available to the public at all reasonable business hours. All departments of the City charged with enforcement of the Comprehensive Plan shall be supplied at the cost of the City, such number of sufficient copies of such ordinance and Comprehensive Plan as may be deemed expedient.

PARAGRAPH 3. This ordinance shall take effect and be in force from and after its publication in the Legal Record, an official City newspaper.

PASSED by the Governing Body this 9th day of February, 2026.

APPROVED AND SIGNED by the Mayor this 9th day of February, 2025.

CITY OF SHAWNEE, KANSAS

By: _____
Michael Sandifer, Mayor

{Seal}

ATTEST:

By: _____
Stephanie Zaldivar, City Clerk

APPROVED AS TO FORM:

By: _____
Jenny Smith, City Attorney

2/17

JOHNSON COUNTY PUBLIC NOTICES

First published in The Legal Record, Tuesday, February 17, 2026.

ORDINANCE NO. 1898

AN ORDINANCE condemning lands or interests in lands for the location, installation, placement, operation, inspection, maintenance, repair and replacement of street lighting, electric structures and lines, water mains and lines, sanitary mains and lines, stormwater collection inlets, mains and lines, telecommunication lines and other public utilities and appurtenances at 6220 Antioch Road; and directing the City Attorney to cause the initiation of eminent domain proceedings as provided by law to acquire the tracts and parcels of land described in this ordinance.

BE IT ORDAINED BY THE CITY COUNCIL OF THE CITY OF MERRIAM, KANSAS:

The following described lands and/or interests in lands are hereby condemned and appropriated to the City of Merriam, Kansas for the location, installation, placement, operation, inspection, maintenance, repair and replacement of street lighting, electric structures and lines, water mains and lines, sanitary mains and lines, stormwater collection inlets, mains and lines, telecommunication lines and other public utilities and appurtenances at 6220 Antioch Road, all within Merriam, Johnson County, Kansas to-wit:

See Exhibit A, which is attached hereto and incorporated herein by reference;

1. It is hereby found that the costs of such project will be paid by the City of Merriam.

2. The City Attorney is hereby ordered and directed forthwith to cause the initiation of proceedings for the acquisition of the above-described real property and/or real property interests and to do and perform all things which might be necessary and required by law to acquire the aforementioned rights in and to said property.

3. This ordinance shall take effect and be in force after its passage, approval and publication.

APPROVED BY THE CITY COUNCIL OF THE CITY OF MERRIAM, KANSAS THIS 9th DAY OF FEBRUARY, 2026.

Bob Pape
Bob Pape
Mayor

ATTEST: Julianna Pinnick
Julianna Pinnick
City Clerk

APPROVED AS TO FORM:
Kathryn Dumovich
~~Ryan Denk~~ Kathryn Dumovich
City Attorney

EXHIBIT 'A'

SHEET 1 OF 2

EASEMENT DESCRIPTION:

A 15 FEET WIDE STRIP OF LAND BEING A PART OF LOT 14, EBY SUBDIVISION, MERRIAM PARK, A SUBDIVISION OF LAND BEING NOW IN THE CITY OF MERRIAM, JOHNSON COUNTY, KANSAS, FILED JUNE 27, 1887 IN THE OFFICE OF THE REGISTER OF DEEDS IN BOOK 2 AT PAGE 10, BEING BOUNDED AND DESCRIBED FOR THE PURPOSES OF AN EVERGY EASEMENT BY OR UNDER THE DIERECT SUPERVISION OF LEE A. HERMRECK, KS PS-1232, UNDER THE AUTHORITY OF MEC CORPORATE CERTIFICATE / LICENSE NO. 336 ON OCTOBER 20, 2025. SAID 15 FEET WIDE STRIP OF LAND LYING IN THE SOUTHWEST QUARTER OF SECTION 12, TOWNSHIP 12 SOUTH, RANGE 24 EAST AND BEING MORE PARTICULARLY DESCRIBED AS FOLLOWS:

BEGINNING AT THE SOUTHEAST CORNER OF AFORESAID LOT 14, BEING ALSO THE POINT OF INTERSECTION OF THE WEST RIGHT-OF-WAY LINE OF ANTIOCH ROAD (PLATTED AS LOOMIS STREET) AS ESTABLISHED 30.00 FEET WEST OF THE EAST LINE OF THE SOUTHEAST QUARTER OF AFORESAID SECTION 12 AND THE NORTH RIGHT-OF-WAY LINE OF W. 62ND TERRACE (PLATTED AS NETTLETON AVENUE) AS NOW ESTABLISHED 60.00 FEET WIDE; THENCE N02°06'46"W ALONG THE EAST LINE OF SAID LOT 14, BEING ALSO ALONG THE WEST RIGHT-OF-WAY-LINE OF SAID ANTIOCH ROAD, A DISTANCE OF 57.92 FEET TO A POINT ON THE SOUTH EDGE OF AN ASPHALT DRIVEWAY; THENCE THE FOLLOWING 2 COURSES ALONG THE SAID ASPHALT DRIVEWAY; THENCE S86°34'29"W DEPARTING SAID WEST RIGHT-OF-WAY LINE OF SAID ANTIOCH ROAD, 2.46 FEET; THENCE S74°12'47"W, 12.40 FEET TO A POINT ON THE EAST FACE OF A CONCRETE WALL; THENCE S03°54'59"E, DEPARTING FROM SAID ASPHALT DRIVEWAY, BEING NOW ALONG THE EAST FACE OF SAID CONCRETE WALL AND ITS SOUTHERLY EXTENSION, 55.04 FEET TO A POINT ON THE SOUTH LINE OF SAID LOT 14, BEING ALSO A POINT ON THE NORTH RIGHT-OF-WAY LINE OF SAID W. 62ND TERRACE; THENCE N87°31'03"E ALONG THE SOUTH LINE OF SAID LOT 14, BEING ALSO ALONG THE NORTH RIGHT-OF-WAY LINE OF SAID W. 62ND TERRACE, A DISTANCE OF 12.77 FEET TO THE POINT OF BEGINNING.

CONTAINING 774 SQUARE FEET, MORE OR LESS.

BASIS OF BEARINGS – KANSAS STATE PLANE COORDINATE SYSTEM, NAD 83, NORTH ZONE.


LEE A. HERMRECK LICENSED LS-1232 KANSAS LAND SURVEYOR
10/22/2025

McCLURE™ making lives better. 1700 SWIFT, SUITE 100 NORTH KANSAS CITY, MISSOURI 816-756-0444 816-756-1673	6220 ANTIOCH ROAD EASEMENT EXHIBIT		EVERGY PROJECT NO. M108621738
	COUNTY, STATE	TRACT NO.	MEC PROJECT NO. 2025000050-097
	JOHNSON COUNTY, KANSAS	PTN 0060	DATE 10/21/2025

EXHIBIT 'A'

SHEET 2 OF 2

THIS SKETCH HAS BEEN PREPARED FOR EASEMENT EXHIBIT PURPOSES ONLY AND DOES NOT CONSTITUTE A BOUNDARY SURVEY. DISTANCES AND BEARINGS ARE BASED ON NAD-83 KANSAS NORTH ZONE, STATE PLANE DATUM.

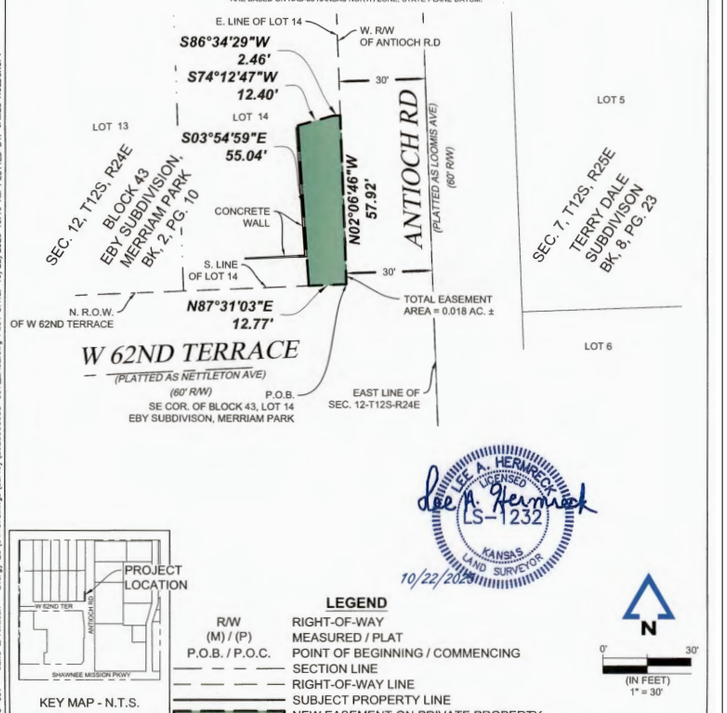

KEY MAP - N.T.S.

LEGEND

R/W	RIGHT-OF-WAY
(M) / (P)	MEASURED / PLAT
P.O.B. / P.O.C.	POINT OF BEGINNING / COMMENCING
	SECTION LINE
	RIGHT-OF-WAY LINE
	SUBJECT PROPERTY LINE
	NEW EASEMENT ON PRIVATE PROPERTY

LEE A. HERMRECK LICENSED LS-1232 KANSAS LAND SURVEYOR
10/22/2025

N
0' 30'
(IN FEET)
1" = 30'

McCLURE™ making lives better. 1700 SWIFT, SUITE 100 NORTH KANSAS CITY, MISSOURI 816-756-0444 816-756-1673	6220 ANTIOCH ROAD EASEMENT EXHIBIT		EVERGY PROJECT NO. M108621738
	COUNTY, STATE	TRACT NO.	MEC PROJECT NO. 2025000050-097
	JOHNSON COUNTY, KANSAS	PTN 0060	DATE 10/21/2025

2/17

JOHNSON COUNTY PUBLIC NOTICES

First published in The Legal Record, Tuesday, February 17, 2026.

ORDINANCE NO. 1897

AN ORDINANCE AUTHORIZING THE SALE, CONSUMPTION, AND POSSESSION OF ALCOHOLIC LIQUOR DURING THE MERRIAM DRIVE LIVE EVENT.

WHEREAS, K.S.A. 41-719 and amendments thereto requires the governing body of the City of Merriam, Kansas ("Governing Body") to approve the consumption of alcoholic liquor at an event held on public streets and sidewalks.

WHEREAS, the City of Merriam, Kansas is sponsoring such event, Merriam Drive Live, on October 3, 2026, from 2 p.m. to 8 p.m. in which a caterer, pursuant to K.S.A. 41-719 and amendments thereto and the Merriam City Code, intends to offer for sale, sell, and serve alcoholic liquor for consumption at the event.

NOW THEREFORE, BE IT ORDAINED BY THE GOVERNING BODY OF THE CITY OF MERRIAM, KANSAS:

SECTION 1: In accordance with K.S.A. 41-719 and amendments thereto, the Governing Body hereby approves the consumption of alcoholic liquor on the street and sidewalks within the boundaries of the permitted area designated on the attached Exhibit A, during the Merriam Drive Live event from 2 p.m. to 8 p.m. on Saturday, October 3, 2026.

SECTION 2: During said periods when consumption of alcoholic liquor is hereby authorized, the areas of the public street designated within the boundaries of the permitted area designated on the attached Exhibit A shall be and are hereby directed to be closed to vehicular traffic.

SECTION 3: During said periods when consumption of alcoholic liquor is hereby authorized, the boundaries of the permitted area designated on the attached Exhibit A shall be clearly marked by signs, a posted map, or other means which reasonably identify the area in which alcoholic liquor may be possessed or consumed at such event.

SECTION 4: This ordinance shall be in full force and effect from and after its passage, approval and publication in the official City newspaper, all as provided by law.

PASSED by the Governing body on this 9 day of February, 2026.

APPROVED AND SIGNED by the Mayor on this 9 day of February, 2026.

Bob Pape

Bob Pape, Mayor

CITY OF MERRIAM SEAL STATE OF KANSAS

(Seal)

ATTEST:

Juliana Pinnick

Juliana Pinnick, City Clerk

APPROVED AS TO FORM:

Kathryn Dumovich

~~Ryan Denk~~, City Attorney

Kathryn Dumovich

EXHIBIT A
BOUNDARY MAP



Merriam Drive Live - Saturday, October 3, 2026

2/17

First published in The Legal Record, Tuesday, February 17, 2026.

VEHICLE AUCTION

First published in The Legal Record Tuesday February 17, 2026. Allied Towing Service impounded vehicles for local police departments and property owners and they will be sold at public (silent bid) auction on February 26, 2026 to the highest bidder unless positive proof of ownership can be presented. All fees must be paid (tow & storage) at the time of pick up. Bids will be accepted between 10:00 am and 2:00 pm and the winning bidder will be notified the following business day. Paperwork $300

2010 Chevrolet Malibu	1G1ZB5EB3AF202640	2003 Honda Civic	2HGES155X3H600083
2011 Kia Sorento	5XYKT3A10BG001266	2016 Kia Sedona	KNDMB5C1XG6134454
1999 Honda Accord	1HGCG5659XA109894	2011 BMW X5	5UXZV4C50BL400423

2/17 2/24

JOHNSON COUNTY PUBLIC NOTICES

First published in The Legal Record, Tuesday, February 17, 2026.

CITY OF LENEXA

NOTICE TO BIDDERS

Sealed bids for 2026 Thoroughfare & Industrial Project will be accepted by the City of Lenexa, Kansas at the Municipal Services Department, 7700 Cottonwood Street, Lenexa, Kansas 66216, until 1:30 pm (local time) on February 25th, 2026 at which time bids will be publicly opened and read aloud at the Lenexa Municipal Services facility. Any bid received after the designated closing time will not be considered and will be returned unopened.

All bids shall be submitted to the Municipal Services Department Customer Service Staff in sealed envelopes addressed to the CITY OF LENEXA, KANSAS, ATTENTION: CITY CLERK, and marked "Bid for: 2026 THOROUGHFARE & INDUSTRIAL PROJECT" Copies of plans, specifications, bidding documents and other Contract Documents are on file at:

Drexel Technologies, Inc.
10840 W. 86th Street
Lenexa, KS 66214

Bidders desiring Contract Documents for use in preparing bids may obtain a set of such documents at the address above.

PLANS AND SPECIFICATIONS MAY BE DOWNLOADED FROM THE DREXEL TECHNOLOGIES, INC. WEBSITE SET FORTH BELOW

https://projectbids.drexeltech.com/

EACH BIDDER WILL BE RESPONSIBLE FOR ENSURING THAT IT HAS RECEIVED ANY AND ALL ADDENDA ISSUED BY CITY IN ACCORDANCE WITH IB-10 OF THE INSTRUCTIONS TO BIDDERS.

CONTRACTORS SHOULD READ AND BE FULLY FAMILIAR WITH ALL CONTRACT DOCUMENTS INCLUDING ADDENDA BEFORE SUBMITTING A BID. IN SUBMITTING A BID, THE BIDDER WARRANTS THAT IT HAS READ THE CONTRACT DOCUMENTS AND IS FULLY FAMILIAR THEREWITH AND THAT IT HAS VISITED THE SITE OF THE WORK TO FULLY INFORM ITSELF AS TO ALL EXISTING CONDITIONS AND LIMITATIONS AND SHALL INCLUDE IN ITS BID A SUM TO COVER THE COST OF ALL ITEMS OF THE WORK AS SPECIFIED IN THE CONTRACT DOCUMENTS.

No oral telegraphic, telephonic proposals or alterations will be considered. Facsimile transmissions will not be accepted.

The following items must be included in the sealed envelope with the Bid:

a. Bid Form;

b. 5% Bid Security--Bid Bond, Cashier's Check or Certified Check (see below); and

c. Acknowledgment of Addenda Issued by City.

Each bidder shall file with its bid a bid bond, a cashier's check or a certified check drawn on an acceptable bank, made payable to City of Lenexa, Kansas, in an amount equal to five percent (5%) of the total bid, which shall be retained by City of Lenexa, Kansas until a Contract for the project has been executed. Bid Bonds will be returned to the bidders, with the exception of the best and lowest and second best and second lowest responsible bidders, within twenty-one (21) days after their bids are rejected. The bid deposit of the lowest and the second lowest responsible bidders will be returned when the Performance Bond, Maintenance Bond and Statutory Bond, each in an amount equal to 100% of the Contract amount; required insurance certificates and other required documents shall have been furnished and the Contract Documents have been executed by the successful bidder.

In the event the low bidder is unable to execute the Contract, for whatever reason, within the time provided in the Notice of Award, City may annul the Notice of Award and the bid deposit may be forfeited and City shall exercise its legal prerogatives, including, but not limited to, enforcement of its rights as to the bid security or specific performance.

City reserves the right to accept or reject any and all bids and to waive any technicalities or irregularities therein. Bids may be modified or withdrawn by written request of the bidder received in the office of City Clerk, prior to the time and date for bid opening.

From and after the release of this Notice, any party intending to bid on the above referenced Project, including their officers, employees, agents, or contractors are specifically prohibited from communicating with any elected or appointed official of the City, directly or indirectly, with regard to the award of the contract for the Project listed above, except as specifically authorized by the Instructions to Bidders. Any such unauthorized communication may result in the automatic disqualification of such bidder.

ALL BIDDERS AGREE THAT REJECTION SHALL CREATE NO LIABILITY ON THE PART OF CITY BECAUSE OF SUCH REJECTION, AND THE FILING OF ANY BID IN RESPONSE TO THIS NOTICE SHALL CONSTITUTE AN AGREEMENT OF THE BIDDER TO THESE CONDITIONS.

If this section is completed, a **Mandatory Pre-Bid Conference** will be held at:

_____, at _____

/s/ Jennifer Martin
Jennifer Martin, City Clerk
City of Lenexa, Kansas

2/17

First published in The Legal Record, Tuesday, February 17, 2026.

CITY OF LENEXA

NOTICE TO BIDDERS

Sealed bids for 2026 PMP UBAS & Overlay Project will be accepted by the City of Lenexa, Kansas at the Municipal Services Department, 7700 Cottonwood Street, Lenexa, Kansas 66216, until 1:00 pm (local time) on February 25, 2026, at which time bids will be publicly opened and read aloud at the Lenexa Municipal Services facility. Any bid received after the designated closing time will not be considered and will be returned unopened.

All bids shall be submitted to the Municipal Services Department Customer Service Staff in sealed envelopes addressed to the CITY OF LENEXA, KANSAS, ATTENTION: CITY CLERK, and marked "Bid for: 2026 UBAS & OVERLAY PROJECT" Copies of plans, specifications, bidding documents and other Contract Documents are on file at:

Drexel Technologies, Inc.
10840 W. 86th Street
Lenexa, KS 66214

Bidders desiring Contract Documents for use in preparing bids may obtain a set of such documents at the address above.

PLANS AND SPECIFICATIONS MAY BE DOWNLOADED FROM THE DREXEL TECHNOLOGIES, INC. WEBSITE SET FORTH BELOW

https://projectbids.drexeltech.com/

EACH BIDDER WILL BE RESPONSIBLE FOR ENSURING THAT IT HAS RECEIVED ANY AND ALL ADDENDA ISSUED BY CITY IN ACCORDANCE WITH IB-10 OF THE INSTRUCTIONS TO BIDDERS.

CONTRACTORS SHOULD READ AND BE FULLY FAMILIAR WITH ALL CONTRACT DOCUMENTS INCLUDING ADDENDA BEFORE SUBMITTING A BID. IN SUBMITTING A BID, THE BIDDER WARRANTS THAT IT HAS READ THE CONTRACT DOCUMENTS AND IS FULLY FAMILIAR THEREWITH AND THAT IT HAS VISITED THE SITE OF THE WORK TO FULLY INFORM ITSELF AS TO ALL EXISTING CONDITIONS AND LIMITATIONS AND SHALL INCLUDE IN ITS BID A SUM TO COVER THE COST OF ALL ITEMS OF THE WORK AS SPECIFIED IN THE CONTRACT DOCUMENTS.

No oral telegraphic, telephonic proposals or alterations will be considered. Facsimile transmissions will not be accepted.

The following items must be included in the sealed envelope with the Bid:

a. Bid Form;

b. 5% Bid Security--Bid Bond, Cashier's Check or Certified Check (see below); and

c. Acknowledgment of Addenda Issued by City.

Each bidder shall file with its bid a bid bond, a cashier's check or a certified check drawn on an acceptable bank, made payable to City of Lenexa, Kansas, in an amount equal to five percent (5%) of the total bid, which shall be retained by City of Lenexa, Kansas until a Contract for the project has been executed. Bid Bonds will be returned to the bidders, with the exception of the best and lowest and second best and second lowest responsible bidders, within twenty-one (21) days after their bids are rejected. The bid deposit of the lowest and the second lowest responsible bidders will be returned when the Performance Bond, Maintenance Bond and Statutory Bond, each in an amount equal to 100% of the Contract amount; required insurance certificates and other required documents shall have been furnished and the Contract Documents have been executed by the successful bidder.

In the event the low bidder is unable to execute the Contract, for whatever reason, within the time provided in the Notice of Award, City may annul the Notice of Award and the bid deposit may be forfeited and City shall exercise its legal prerogatives, including, but not limited to, enforcement of its rights as to the bid security or specific performance.

City reserves the right to accept or reject any and all bids and to waive any technicalities or irregularities therein. Bids may be modified or withdrawn by written request of the bidder received in the office of City Clerk, prior to the time and date for bid opening.

From and after the release of this Notice, any party intending to bid on the above referenced Project, including their officers, employees, agents, or contractors are specifically prohibited from communicating with any elected or appointed official of the City, directly or indirectly, with regard to the award of the contract for the Project listed above, except as specifically authorized by the Instructions to Bidders. Any such unauthorized communication may result in the automatic disqualification of such bidder.

ALL BIDDERS AGREE THAT REJECTION SHALL CREATE NO LIABILITY ON THE PART OF CITY BECAUSE OF SUCH REJECTION, AND THE FILING OF ANY BID IN RESPONSE TO THIS NOTICE SHALL CONSTITUTE AN AGREEMENT OF THE BIDDER TO THESE CONDITIONS.

If this section is completed, a **Mandatory Pre-Bid Conference** will be held at:

_____, at _____

/s/ Jennifer Martin
Jennifer Martin, City Clerk
City of Lenexa, Kansas

2/17

JOHNSON COUNTY PUBLIC NOTICES

First published in The Legal Record, Tuesday, February 17, 2026.

VEHICLE AUCTION
SIMPLE TOW
313 W. ELM ST.
OLATHE, KS 66061
913-669-0411
AUCTION DATE: MARCH 4TH, 2026 AT 10AM. LIVE AUCTION OPEN TO THE PUBLIC.
PURSUANT TO K.S.A. 8-1102 AND K.S.A 58-211 THE VEHICLES WILL BE SOLD AT AUCTION ON MARCH 4TH, 2026 AT 10AM UNLESS CLAIMED BY THE OWNER AND ALL TOW AND STORAGE CHARGES ARE PAID IN FULL. ALL SALES ARE FINAL. NO REFUNDS. ALL SALES ARE "AS IS".

2009 Hyundai ELANTRA
KMHDU46D79U625066

2009 Chrysler PT Cruiser
3A8FY48969T532889

2015 Nissan Altima
1N4AL3AP7FN395465

2009 Kia Spectra
KNAFE222095663698

2020 Hyundai VELOSTER
KMHT36AH3LU005018

2006 Honda Accord
1HGCM56466A175057

2012 MINI Cooper Countryman
WMWZC3C55CWL84377
2/17 2/24

First published in The Legal Record, Tuesday, February 17, 2026.

CITY OF OLATHE, KANSAS

ENGINEERING DIVISION

NOTICE TO BIDDERS

Sealed bids will be received online at olatheks.bonfirehub.com, until 10:00 a.m. local time, on Tuesday, March 10, 2026, for the construction of the 2026 MAQS Micro Surface Project, Project No. 3-P-008-26.

At said time and place, and promptly thereafter, all bids that have been duly received will be publicly opened online at olatheks.bonfirehub.com.

The work consists of the following:

Modified Aggregate Quickset Surface (MAQS) treatment on one hundred thirty-eight (138) local and collector streets and cul-de-sacs, totaling approximately 432,152 square yards of surface treatment and replacement of pavement markings.

Bid documents including drawings and specifications are on file at the office of Public Works of Olathe, Kansas, and are open for public inspections. Bid documents and drawings may be downloaded free of charge from olatheks.bonfirehub.com. Only bids submitted electronically at olatheks.bonfirehub.com will be accepted.

An Owner's Contingency Allowance determined by the City will be included within the Schedule of Values for this project, following the bid opening.

A satisfactory bid bond executed by the bidder or an acceptable surety, in an amount equal to five percent (5%) of the total bid for work shall be submitted with each proposal. A scanned copy of the BID BOND must be included with the online bid submitted at olatheks.bonfirehub.com. The original copy of the BID BOND form must be submitted to the ENGINEER within 48 hours of bid opening. Failure to submit original copy of the bid bond will result in rejection of bid and OWNER's selection of the next low qualified bidder.

The successful bidder will be required to furnish and pay satisfactory performance and payment bond or bonds.

The City of Olathe, Kansas, reserves the right to reject any or all bids or to waive any informality in the bidding.

Bids may be held by the City of Olathe, Kansas, for a period not to exceed sixty (60) days from the date of the opening of bids for the purpose of reviewing the bids and investigating the qualifications of bidders, prior to awarding the contract.

City of Olathe, Kansas

BY Brenda Swearingian
City Clerk

2/17